


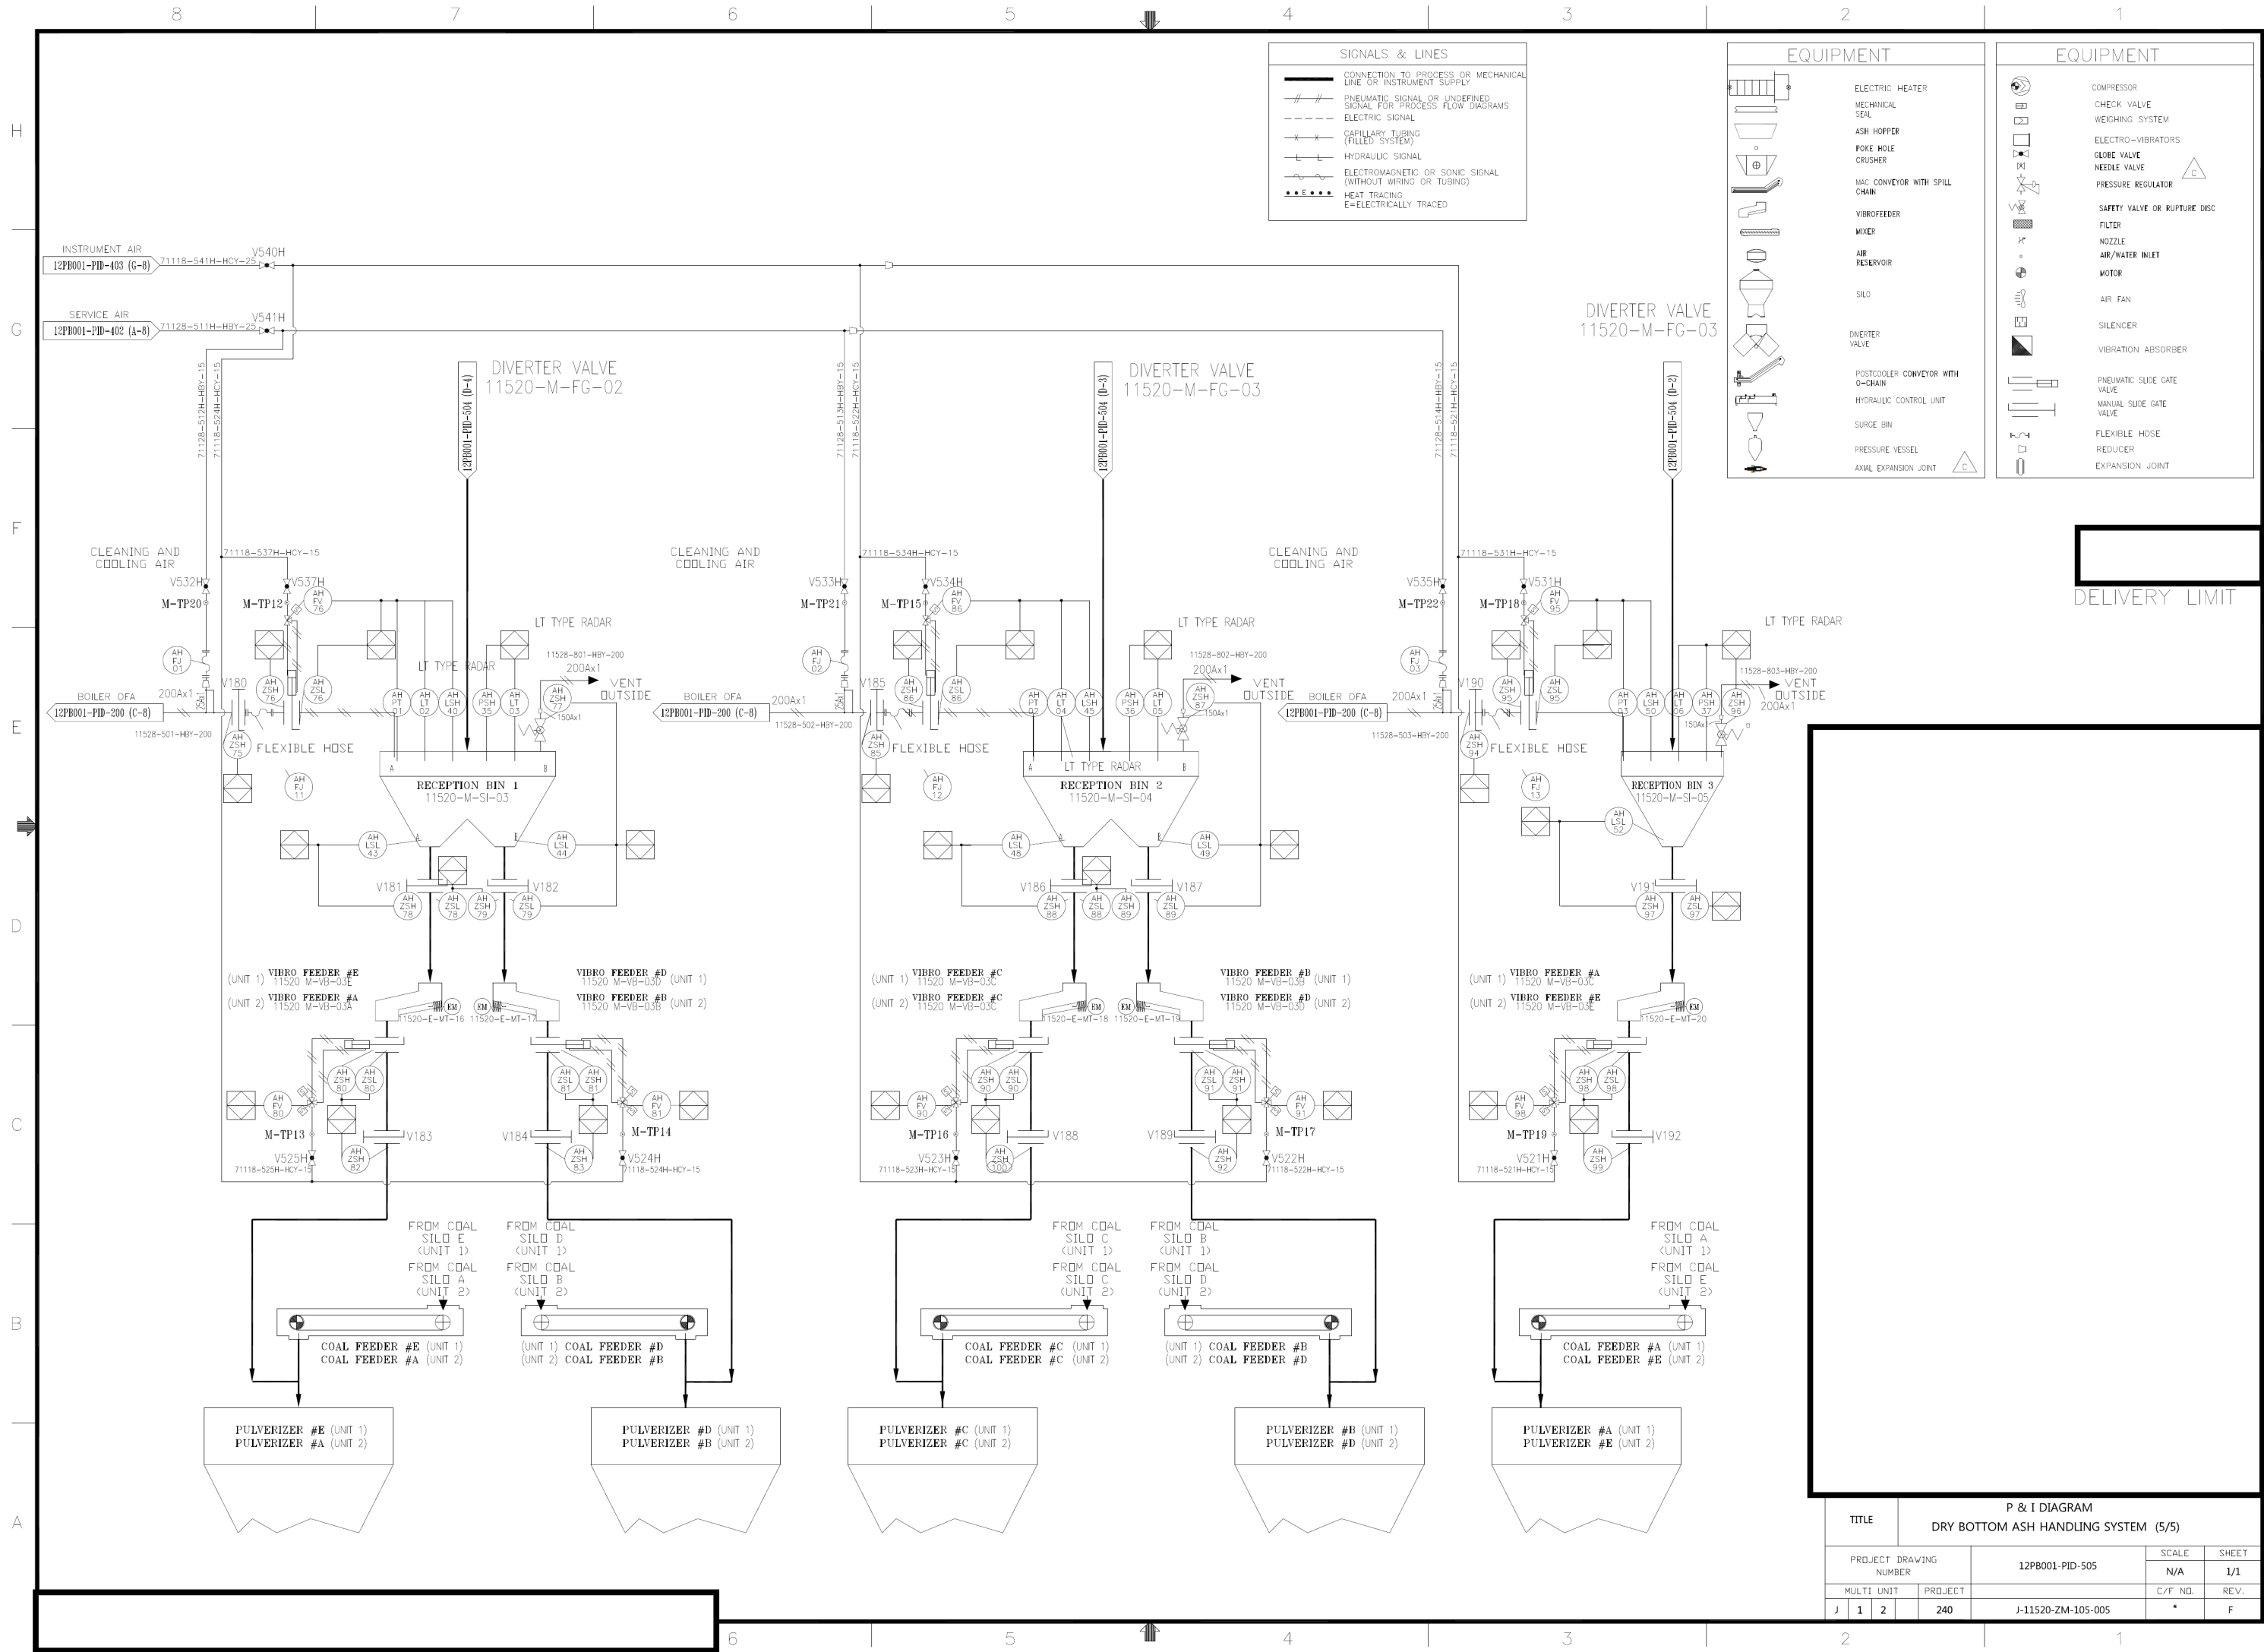

P & I DIAGRAM				
DRY BOTTOM ASH HANDLING SYSTEM (5/5)				
PROJECT DRAWING NUMBER		12PB001-PID-505	SCALE	N/A
MULTI UNIT		240	C/F NO.	1/1
J		1 2	REV.	F