


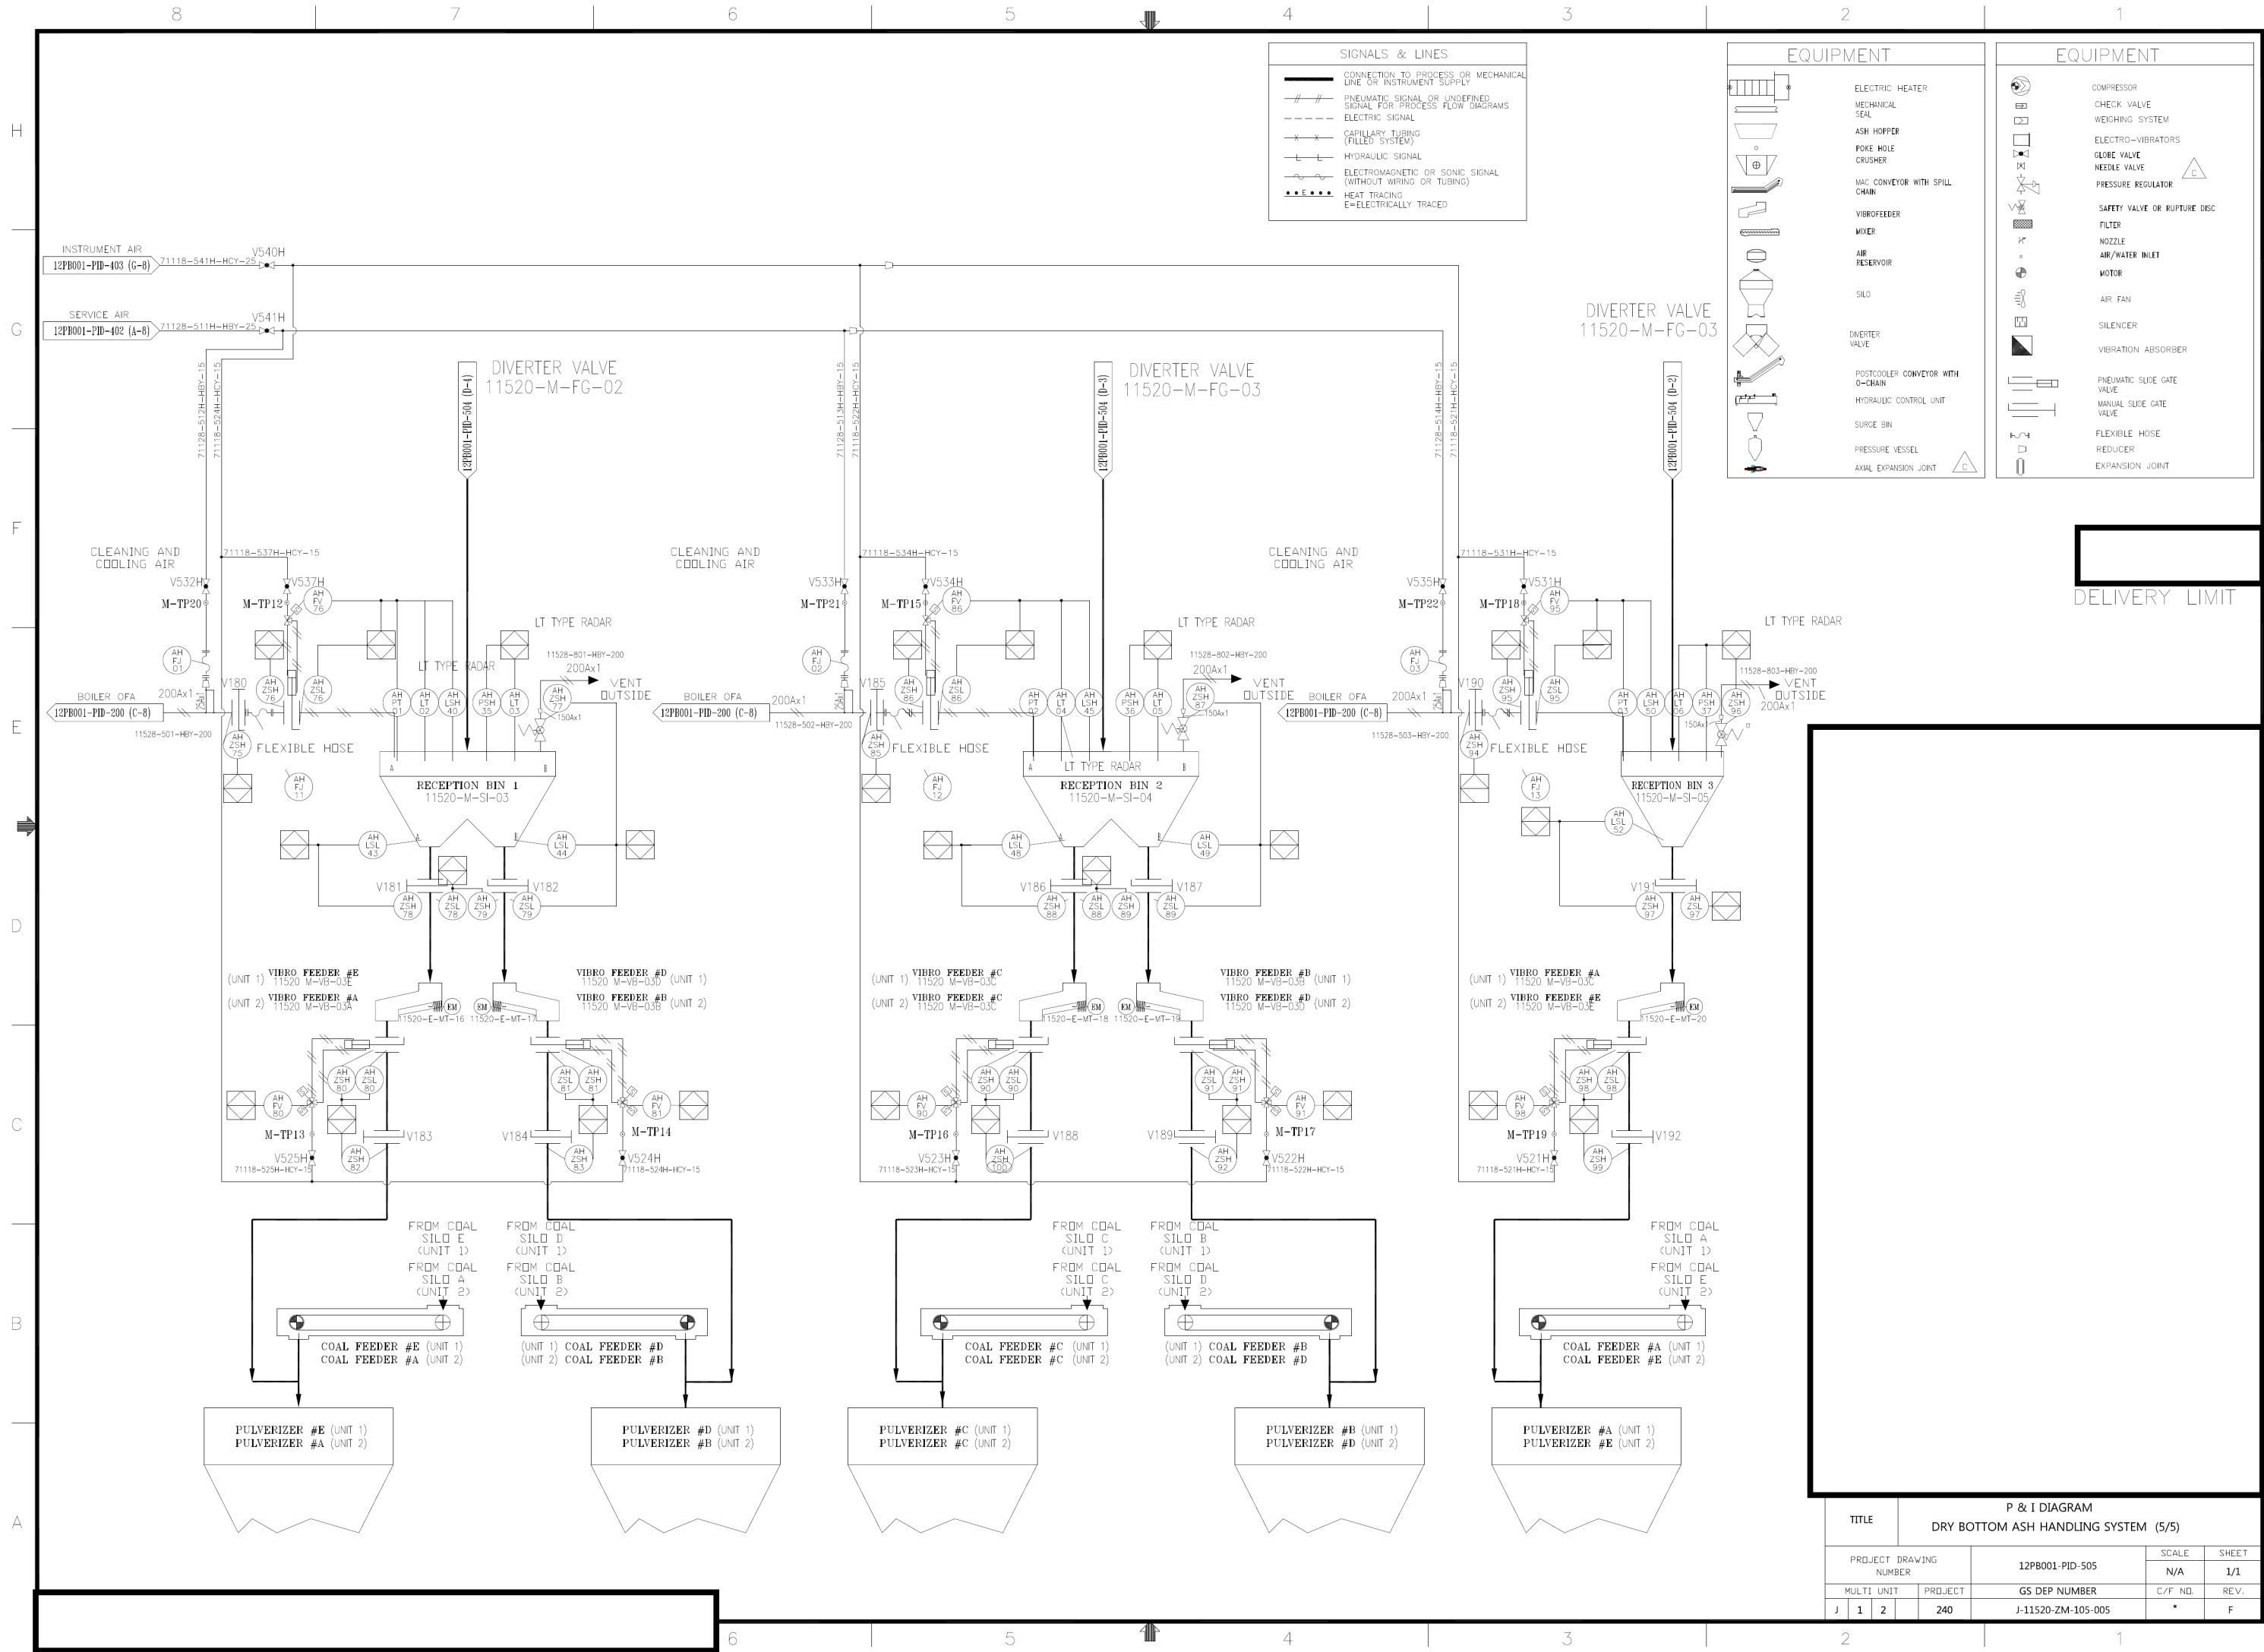

P & I DIAGRAM DRY BOTTOM ASH HANDLING SYSTEM (5/5)				
TITLE		PROJECT DRAWING NUMBER		SHEET
		12PB001-PID-505		N/A
MULTI UNIT		PROJECT		REV.
J 1 2		240		F
		GS DEP NUMBER		C/F NO.
		J-11520-ZM-105-005		*