


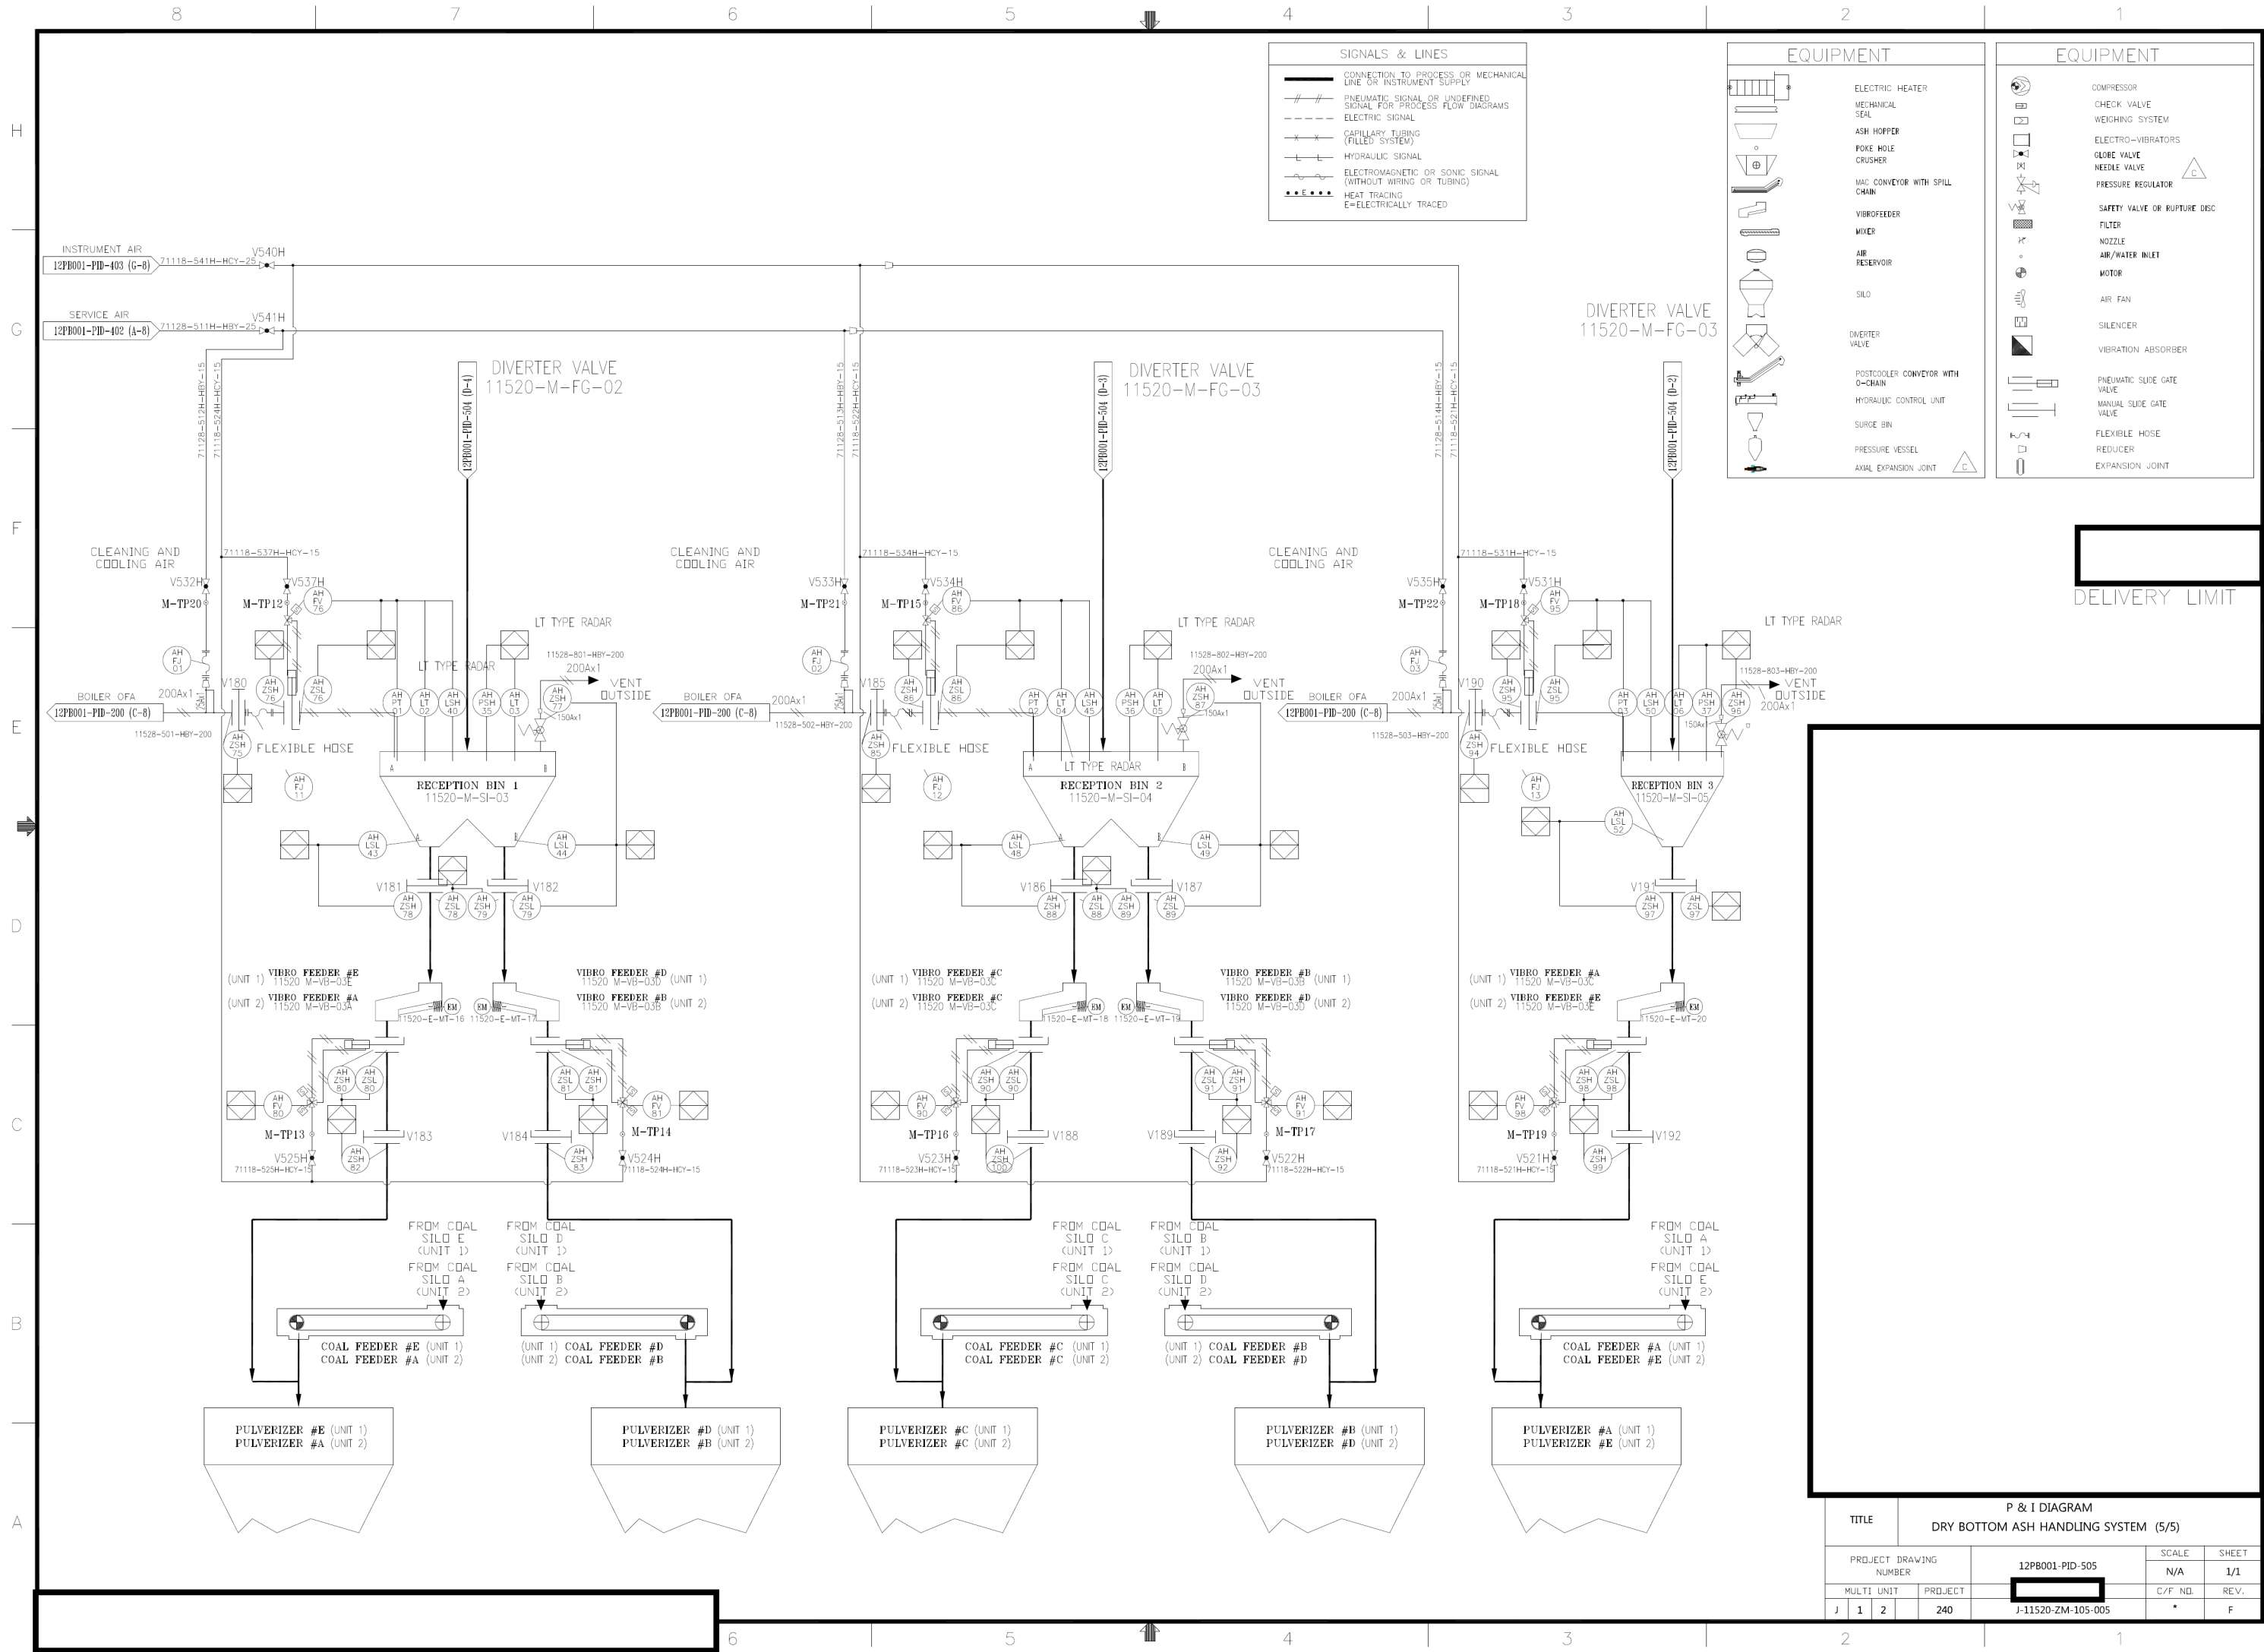

SIGNALS & LINES


- CONNECTION TO PROCESS OR MECHANICAL LINE OR INSTRUMENT SUPPLY
- PNEUMATIC SIGNAL OR UNDEFINED SIGNAL FOR PROCESS FLOW DIAGRAMS
- - - - - ELECTRIC SIGNAL
- x - x - CAPILLARY TUBING (FILLED SYSTEM)
- L - L - HYDRAULIC SIGNAL
- ~ - ~ - ELECTROMAGNETIC OR SONIC SIGNAL (WITHOUT WIRING OR TUBING)
- - HEAT TRACING
- E - E - ELECTRICALLY TRACED

EQUIPMENT

- ELECTRIC HEATER
- MECHANICAL SEAL
- ASH HOPPER
- POKE HOLE
- CRUSHER
- MAC CONVEYOR WITH SPILL CHAIN
- VIBROFEEDER
- MIXER
- AIR RESERVOIR
- SILLO
- DIVERTER VALVE
- POSTCOOLER CONVEYOR WITH O-CHAIN
- HYDRAULIC CONTROL UNIT
- SURGE BIN
- PRESSURE VESSEL
- AXIAL EXPANSION JOINT

EQUIPMENT

- COMPRESSOR
- CHECK VALVE
- WEIGHING SYSTEM
- ELECTRO-VIBRATORS
- GLOBE VALVE
- NEEDLE VALVE
- PRESSURE REGULATOR
- SAFETY VALVE OR RUPTURE DISC
- FILTER
- NOZZLE
- AIR/WATER INLET
- MOTOR
- AIR FAN
- SILENCER
- VIBRATION ABSORBER
- PNEUMATIC SLIDE GATE VALVE
- MANUAL SLIDE GATE VALVE
- FLEXIBLE HOSE
- REDUCER
- EXPANSION JOINT

 

TITLE		P & I DIAGRAM DRY BOTTOM ASH HANDLING SYSTEM (5/5)			
PROJECT DRAWING NUMBER		12PB001-PID-505	SCALE	SHEET	
MULTI UNIT		240	N/A	1/1	
J	1	2	C/F NO.	REV.	
			*	F	